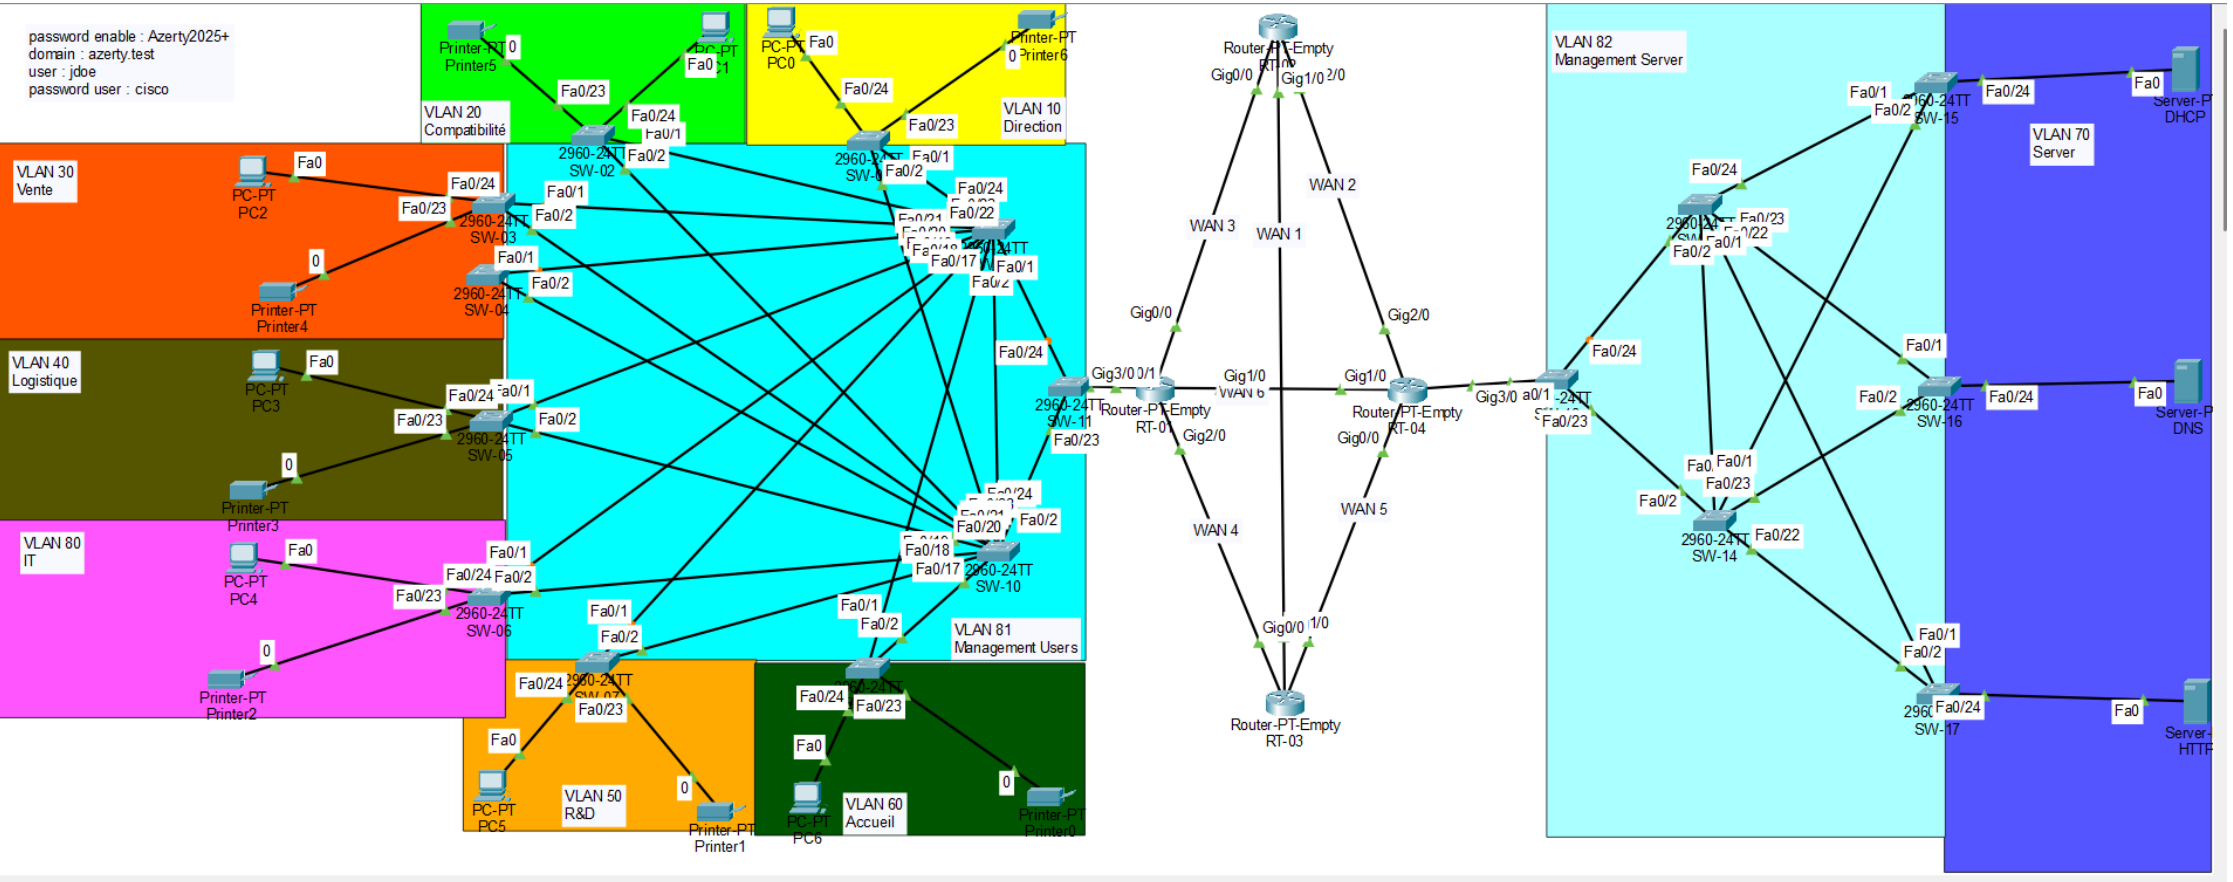
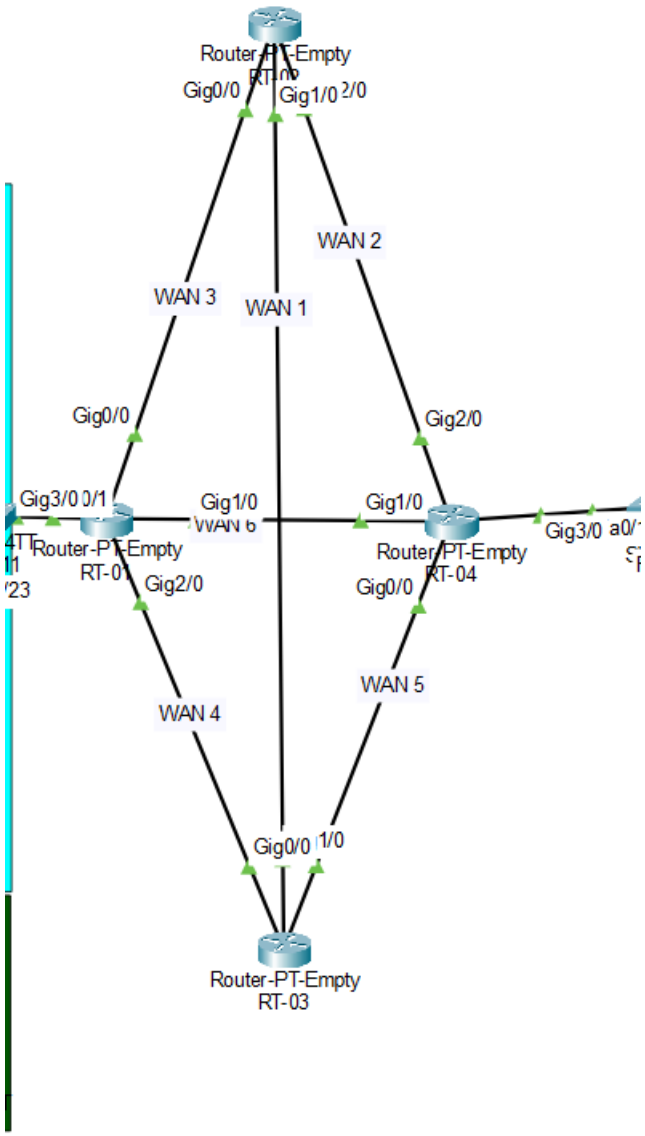
Zone	VLAN	Réseau CIDR	Gateway	Mode
Dept-A	30	192.168.0.0/26	192.168.0.1	DHCP
Dept-B	20	192.168.0.64/27	192.168.0.65	DHCP
Dept-C	40	192.168.0.96/27	192.168.0.97	DHCP
Dept-D	80	192.168.0.128/27	192.168.0.129	DHCP
Dept-E	50	192.168.0.160/27	192.168.0.161	DHCP
Dept-F	10	192.168.0.192/27	192.168.0.193	DHCP
MGMT-USERS	81	192.168.0.224/28	192.168.0.225	
MGMT-SERVERS	82	192.168.0.240/28	192.168.0.241	
SRV-ZONE	70	192.168.1.0/29	192.168.1.1	DHCP
Dept-G	60	192.168.1.8/29	192.168.1.9	DHCP
WAN 1	-	192.168.1.16/30	-	Statique
WAN 2	-	192.168.1.20/30	-	Statique
WAN 3	-	192.168.1.24/30	-	Statique
WAN 4	-	192.168.1.28/30	-	Statique
WAN 5	-	192.168.1.32/30	-	Statique
WAN 6	-	192.168.1.36/30	-	Statique


Type	Nom	VLAN	IP
PC	PC-A-01	Dept-A	DHCP
PC	PC-B-01	Dept-B	DHCP
PC	PC-C-01	Dept-C	DHCP
PC	PC-D-01	Dept-D	DHCP
PC	PC-E-01	Dept-E	DHCP
PC	PC-F-01	Dept-F	DHCP
PC	PC-G-01	Dept-G	DHCP
Imprimante	PRN-A-01	Dept-A	-
Imprimante	PRN-B-01	Dept-B	-
Imprimante	PRN-C-01	Dept-C	-
Imprimante	PRN-D-01	Dept-D	-
Imprimante	PRN-E-01	Dept-E	-
Imprimante	PRN-F-01	Dept-F	-
Imprimante	PRN-G-01	Dept-G	-
Serveur	SRV-DHCP-01	SRV-ZONE	192.168.1.2
Serveur	SRV-DNS-01	SRV-ZONE	192.168.1.3
Serveur	SRV-HTTP-01	SRV-ZONE	192.168.1.4
Switch	SW-MGU-01	MGMT-USERS	192.168.0.226


Type	Nom	VLAN	IP
Switch	SW-MGU-02	MGMT-USERS	192.168.0.227
Switch	SW-MGU-03	MGMT-USERS	192.168.0.228
Switch	SW-MGU-04	MGMT-USERS	192.168.0.229
Switch	SW-MGU-05	MGMT-USERS	192.168.0.230
Switch	SW-MGU-06	MGMT-USERS	192.168.0.231
Switch	SW-MGU-07	MGMT-USERS	192.168.0.232
Switch	SW-MGU-08	MGMT-USERS	192.168.0.233
Switch	SW-MGU-09	MGMT-USERS	192.168.0.234
Switch	SW-MGU-10	MGMT-USERS	192.168.0.235
Switch	SW-MGU-11	MGMT-USERS	192.168.0.236
Switch	SW-MGS-01	MGMT-SERVERS	192.168.0.242
Switch	SW-MGS-02	MGMT-SERVERS	192.168.0.243
Switch	SW-MGS-03	MGMT-SERVERS	192.168.0.244
Switch	SW-MGS-04	MGMT-SERVERS	192.168.0.245
Switch	SW-MGS-05	MGMT-SERVERS	192.168.0.246
Switch	SW-MGS-06	MGMT-SERVERS	192.168.0.247
Routeur	RT-MID-01	WAN 3,4,6	-
Routeur	RT-MID-02	WAN 1,2,3	-

Type	Nom	VLAN	IP
Routeur	RT-MID-03	WAN 4,5,6	-
Routeur	RT-MID-04	WAN 2,5,6	-


password enable : Azerty2025+
domain : azerty.test
user : jdoe
password user : cisco
VLAN 20
Compatibilité
VLAN 10
Direction
VLAN 30
Vente
VLAN 40
Logistique
VLAN 80
IT
VLAN 81
Management Users
VLAN 50
R&D
VLAN 60
Accueil
VLAN 82
Management Server
VLAN 70
Server
Router-PT-Empty
RT-01
Router-PT-Empty
RT-04
Router-PT-Empty
RT-03
WAN 1
WAN 2
WAN 3
WAN 4
WAN 5
2960-24TT
SW-02
SW-03
SW-04
SW-05
SW-06
SW-10
SW-11
SW-14
SW-15
SW-16
SW-17
PC-PT
PC0
PC2
PC3
PC4
PC5
PC6
Printer-PT
Printer0
Printer1
Printer2
Printer3
Printer4
Printer5
Printer6
Server-PT
DHCP
DNS
HTTP


Router-PT-Empty
RT-00
Gig0/0
Gig1/0
WAN 2
WAN 3
WAN 1
Gig0/0
Gig2/0
Gig3/0
Gig1/0
Router-PT-Empty
RT-01
Gig2/0
Gig0/0
Router-PT-Empty
RT-04
WAN 4
WAN 5
Gig0/0
Router-PT-Empty
RT-03

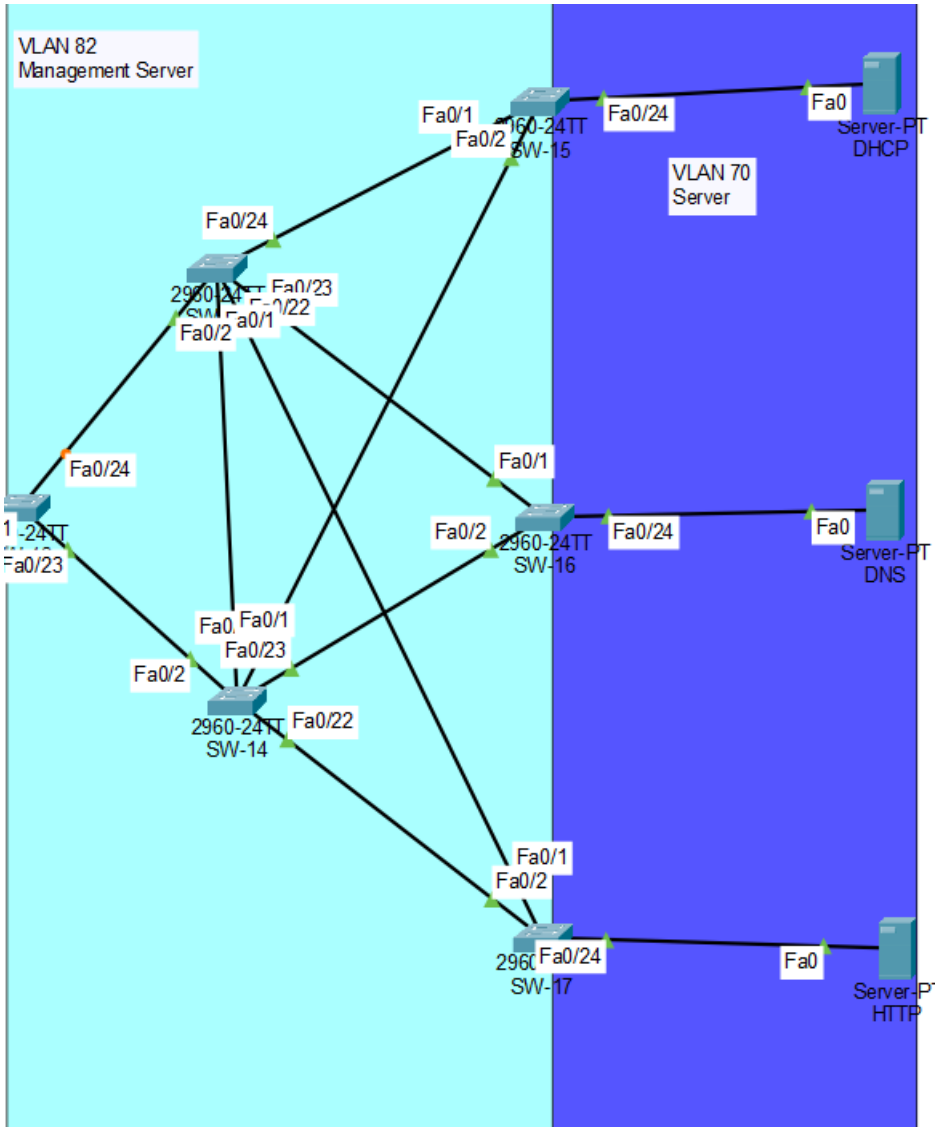
VLAN 82
Management Server
VLAN 70
Server
Fa0/1
Fa0/2
Fa0/24
Fa0
Server-PT
DHCP
Fa0/24
Fa0/23
Fa0/22
Fa0/1
Fa0/2
Fa0/24
Fa0/1
Fa0/2
2960-24TT
SW-16
Fa0/24
Fa0
Server-PT
DNS
Fa0/23
Fa0/1
Fa0/2
Fa0/23
2960-24TT
SW-14
Fa0/22
Fa0/1
Fa0/2
Fa0/24
Fa0
Server-PT
HTTP

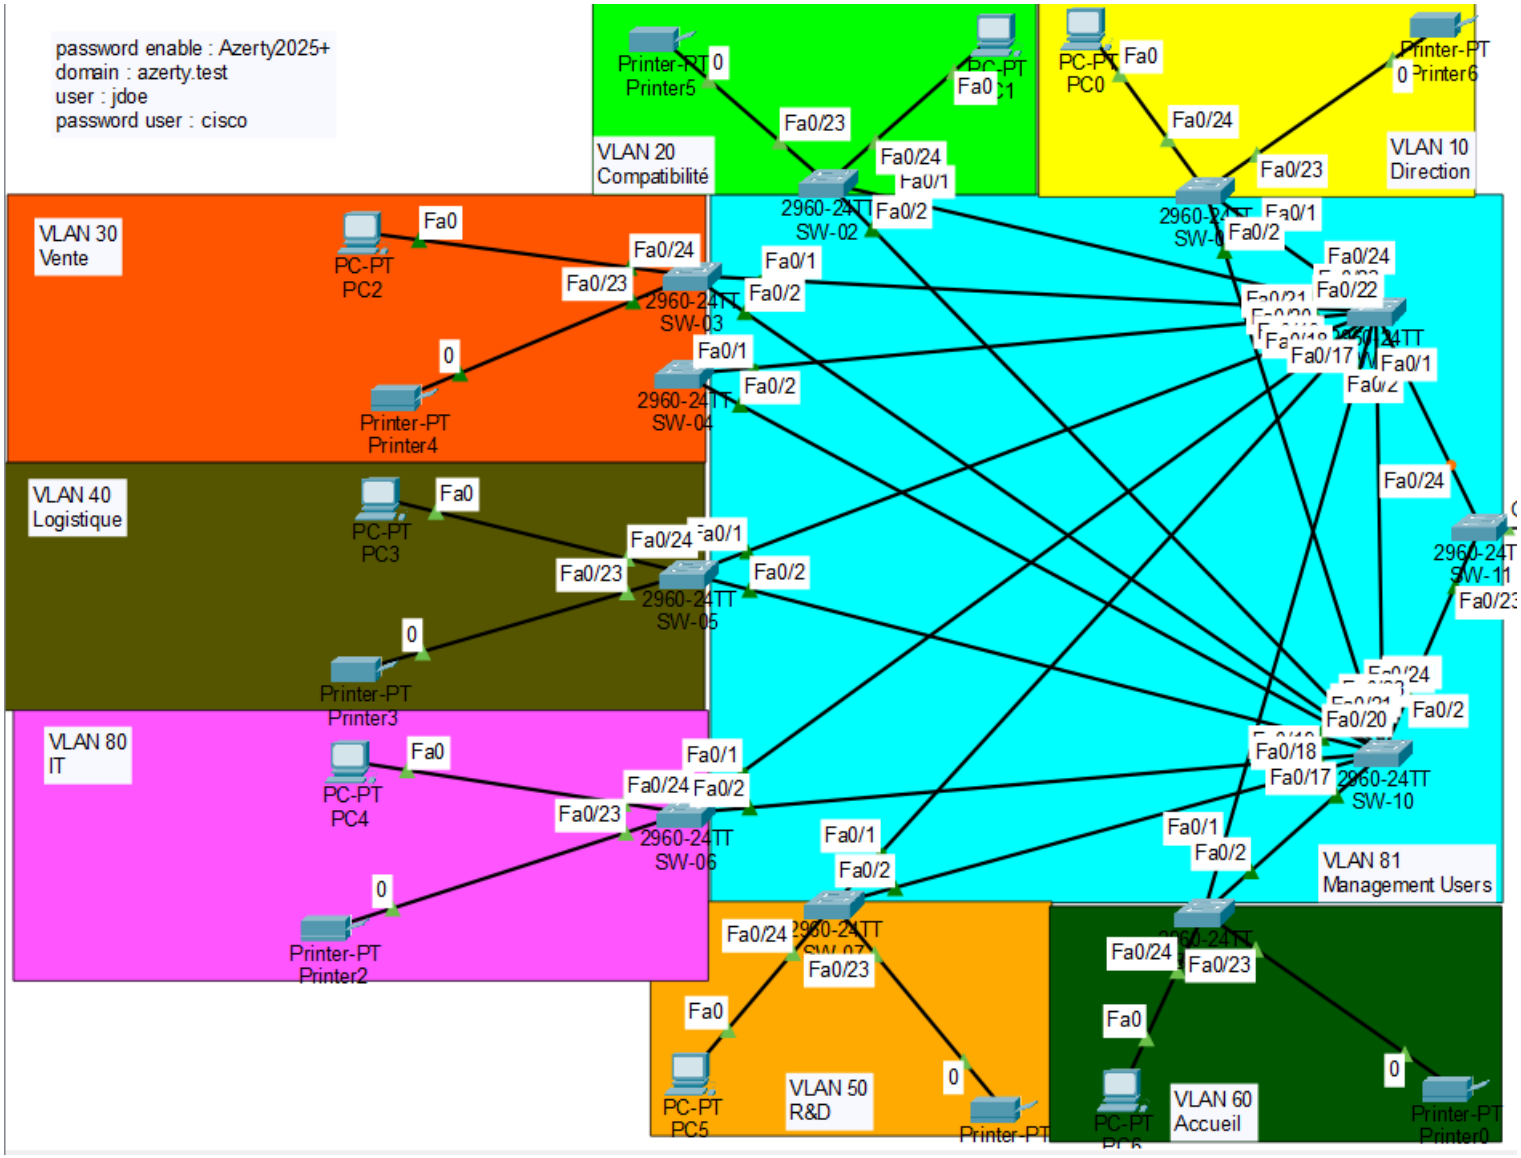
password enable : Azerty2025+
domain : azerty.test
user : jdoe
password user : cisco
VLAN 20
Compatibilité
VLAN 10
Direction
VLAN 30
Vente
VLAN 40
Logistique
VLAN 80
IT
VLAN 81
Management Users
VLAN 50
R&D
VLAN 60
Accueil
PC-PT PC0
PC-PT PC2
PC-PT PC3
PC-PT PC4
PC-PT PC5
Printer-PT Printer5
Printer-PT Printer6
Printer-PT Printer4
Printer-PT Printer3
Printer-PT Printer2
Printer-PT Printer0
2960-24TT SW-02
2960-24TT SW-03
2960-24TT SW-04
2960-24TT SW-05
2960-24TT SW-06
2960-24TT SW-10
2960-24T SW-11
Fa0
Fa0/1
Fa0/2
Fa0/17
Fa0/18
Fa0/20
Fa0/22
Fa0/23
Fa0/24
0